PROVINCIA DE BUENOS AIRES
MINISTERIO DE ECONOMÍA
Dirección Provincial de Catastro Territorial

CATASTRO PARCELARIO

PARTIDO: GRAL. PINTO

000179

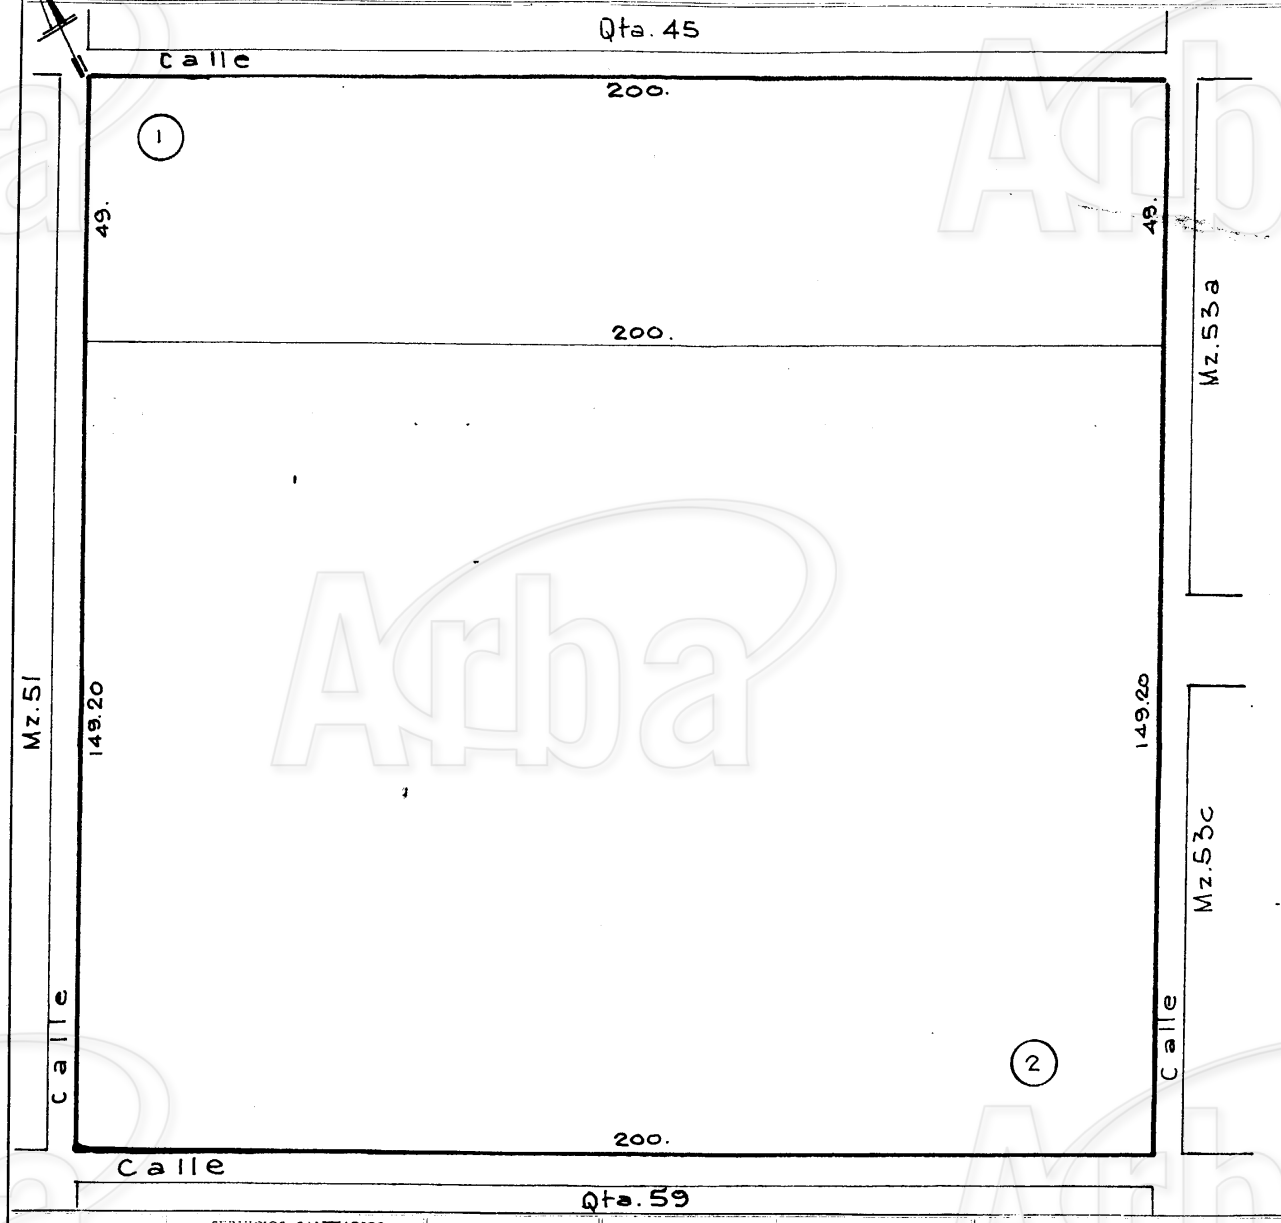

UBICACIÓN

CATASTRO

CIRCUNS. I
SECCION B
CHACRA
QUINTA 52
FRACCION
MANZANA
TITULO

SUPERFICIES

Parc.	Superficie	Parc.	Superficie
1	9.800.		
2	29.840.		

SUP. TOTAL:

CALLES	SERVICIOS SANITARIOS				AFIRMADOS	MEJORAS	MUNICIPALES	PLANOS
	AGUA	FECHA	CLOA.	FECHA				ORIGEN:

ESCALA 1:1000 REP. DE PLANO 15 - 81 PLANO C 91 ANCS

PLANCHETA DIGITAL

Partido 44
General Pinto

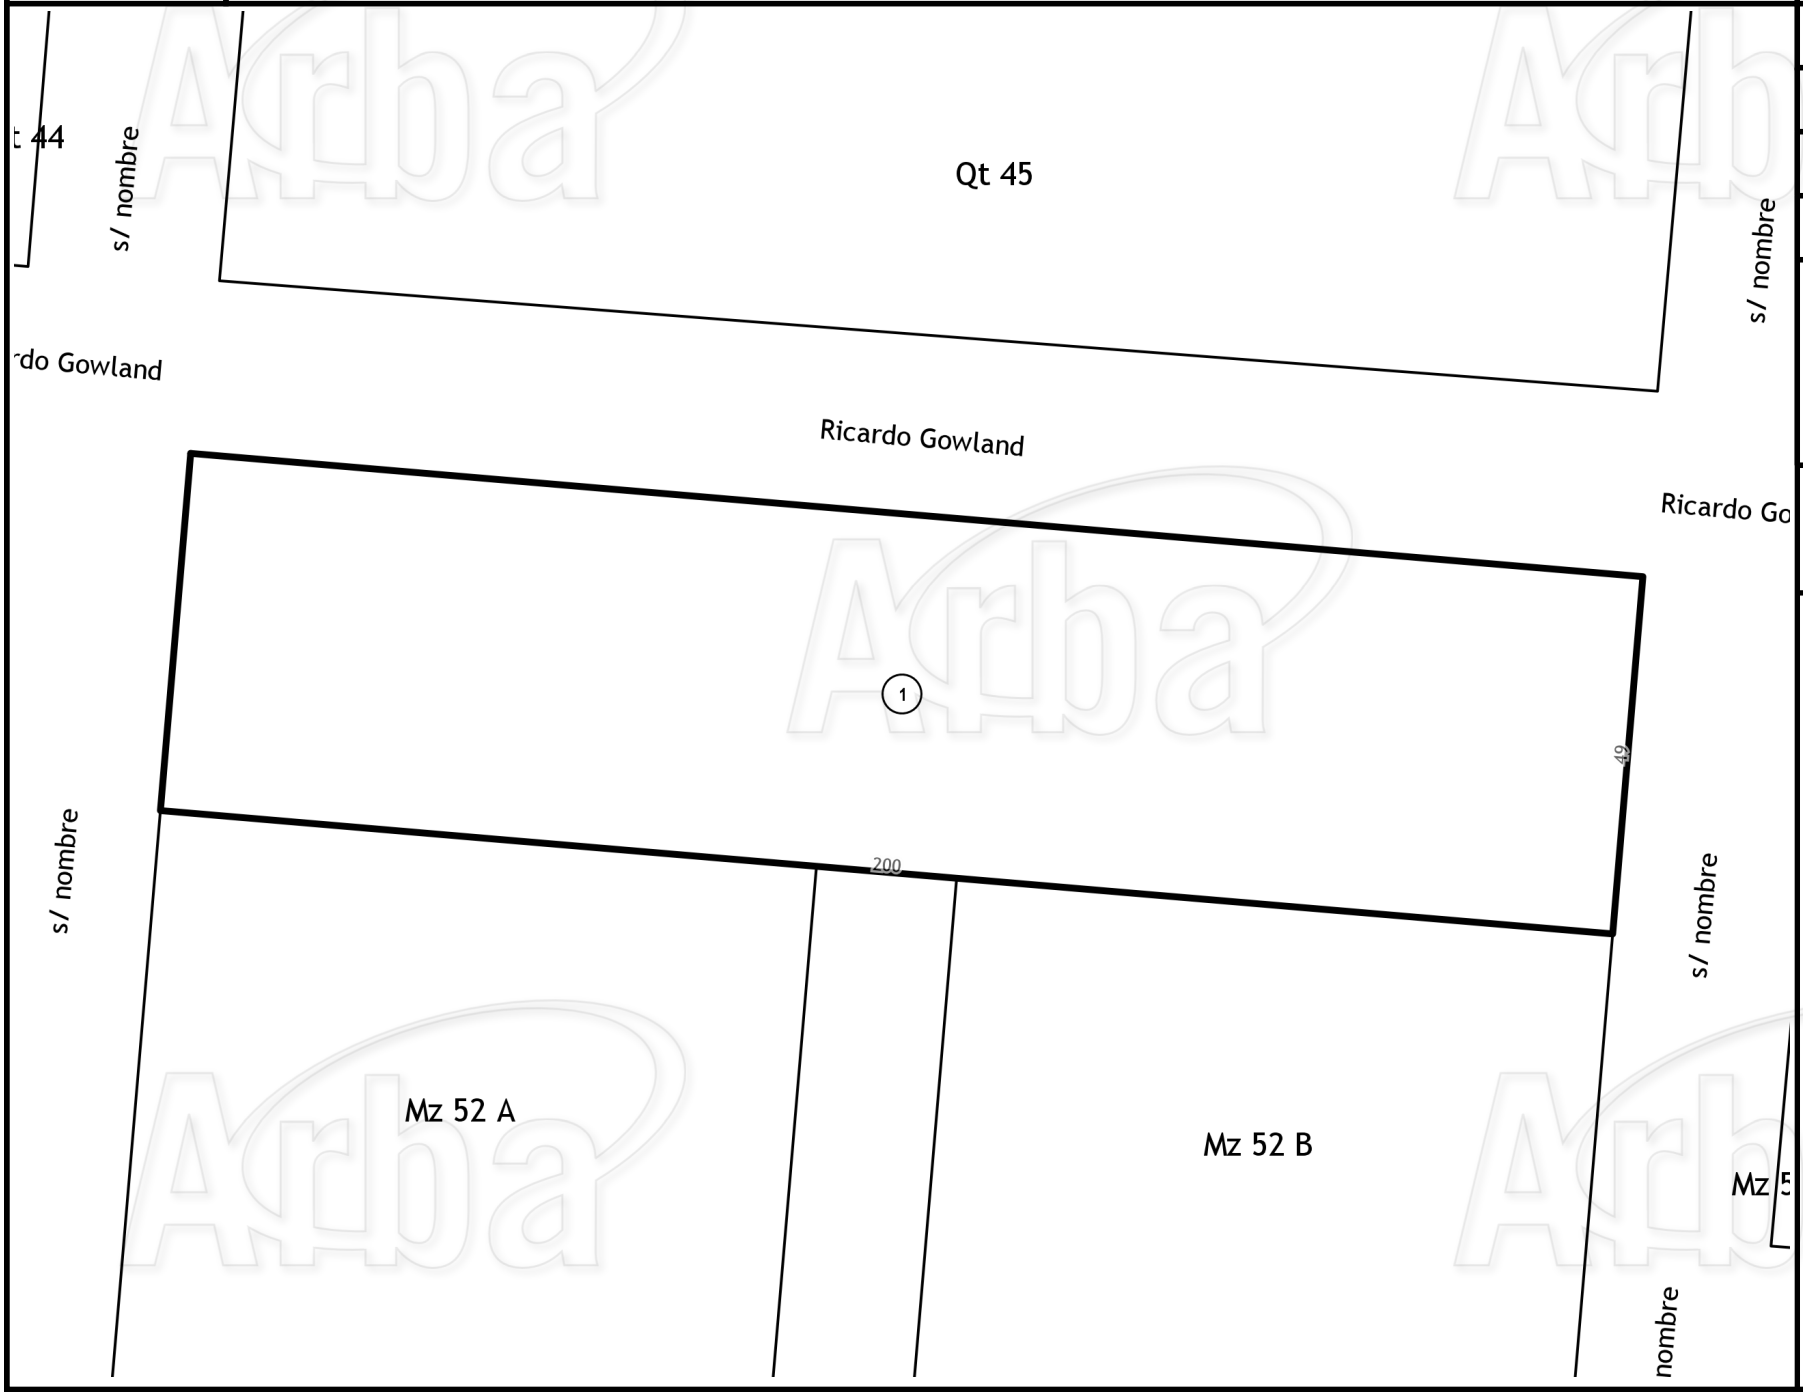

NOMENCLATURA

Cir. 1	Sec. B
Ch.	Qt. 52
Fr.	Mz.

N
W E
S

Parcela baldía según catastro