# PARTIDO DE GRAL. PINTO

**Circunscripción I**
**Sección A**
**Manzana 82**

Manzana 82 s/titulo.

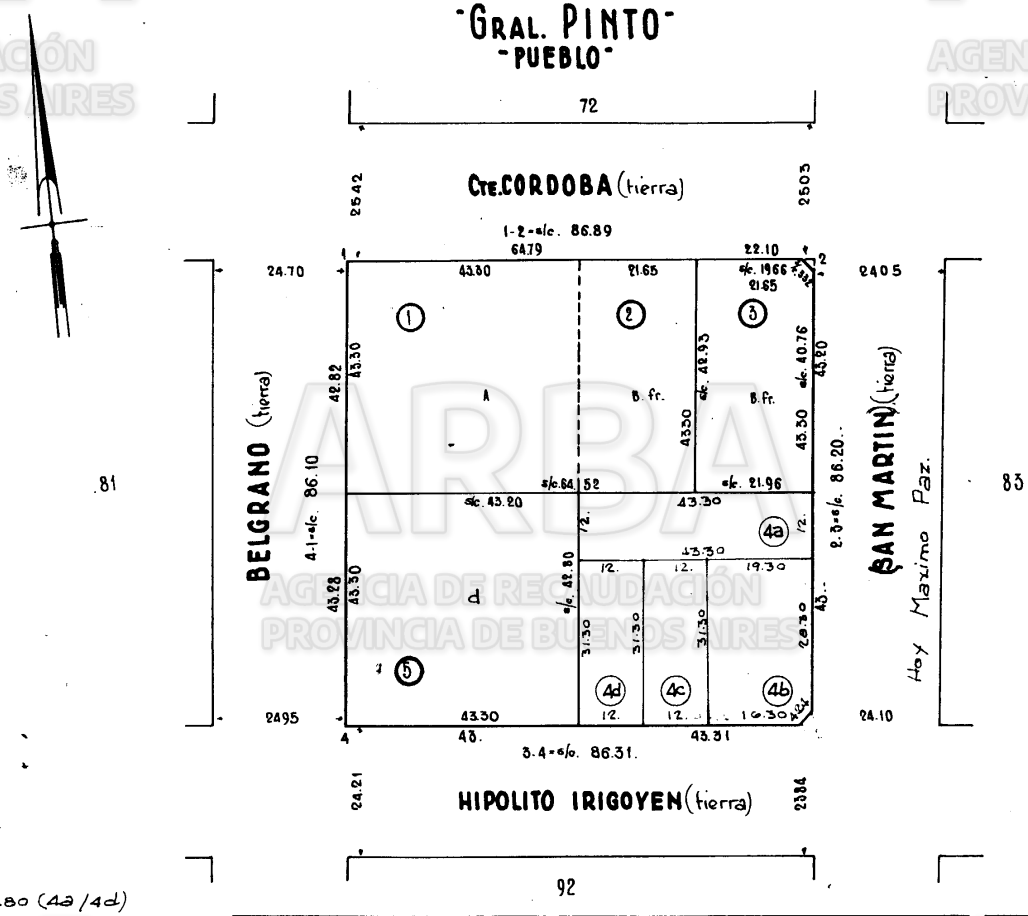


| PARCELA | LOTE | SUPERFICIE M² S/T | | S/P | | S/C | | Nº DE GUÍA |
|---|---|---|---|---|---|---|---|---|
| 1 | A | 1874 | 89 | | | | | |
| 2 | B.fr. | 937 | 45 | | | | | |
| 3 | B.fr. | 937 | 44 | | | 945 | 74 | |
| ~~4~~ | ~~C~~ | ~~1874~~ | ~~89~~ | | | ~~1857~~ | ~~36~~ | |
| 5 | D | 1874 | 89 | | | 1855 | 02 | |
| 4a | | | | 519 | 60 | | | |
| 4b | | | | 599 | 59 | | | |
| 4c | | | | 375 | 60 | | | |
| 4d | | | | 375 | 60 | | | |
| SUP. GENERALES | | S/T 7499 | 56 | S/P | | S/C | | |

44-28-80 (4a/4d)

PLANO GENERAL AGREGADO

Reg. de la P.
Geod. y Catastro Dupl: 25
Escribano
Otras fuentes

Estudiada 16-4-41
Medida 23-1-41

Escala 1: 1.000

| SERVICIOS PUBLICOS | | | | | | DISTANCIAS PRINCIPALES | | | | |
|---|---|---|---|---|---|---|---|---|---|---|
| CALLE | Alumbr. | Barrido | Limpi. | Cloac. | Ag. Cte. | Tranvia | Omn. o Cole. | Escuela | Est. F.C. | Afirmado |
| Cte. Cordoba | – | – | – | – | – | – | 4. c. | 6. c. | 6. c. | – |
| San Martin | – | – | – | – | – | – | " " | " " | " " | – |
| H. Irigoyen | – | – | – | – | – | – | " " | " " | " " | – |
| Belgrano | – | – | – | – | – | – | " " | " " | " " | – |

ANGULOS

F. y E. GARCIA OLANO - J. M. RAGGIO - E. A. PODESTÁ
Ings. Civiles

Dib. 12-8-(88)

ARBA AGENCIA DE RECAUDACIÓN PROVINCIA DE BUENOS AIRES

# PLANCHETA DIGITAL

**Partido 44**
**General Pinto**

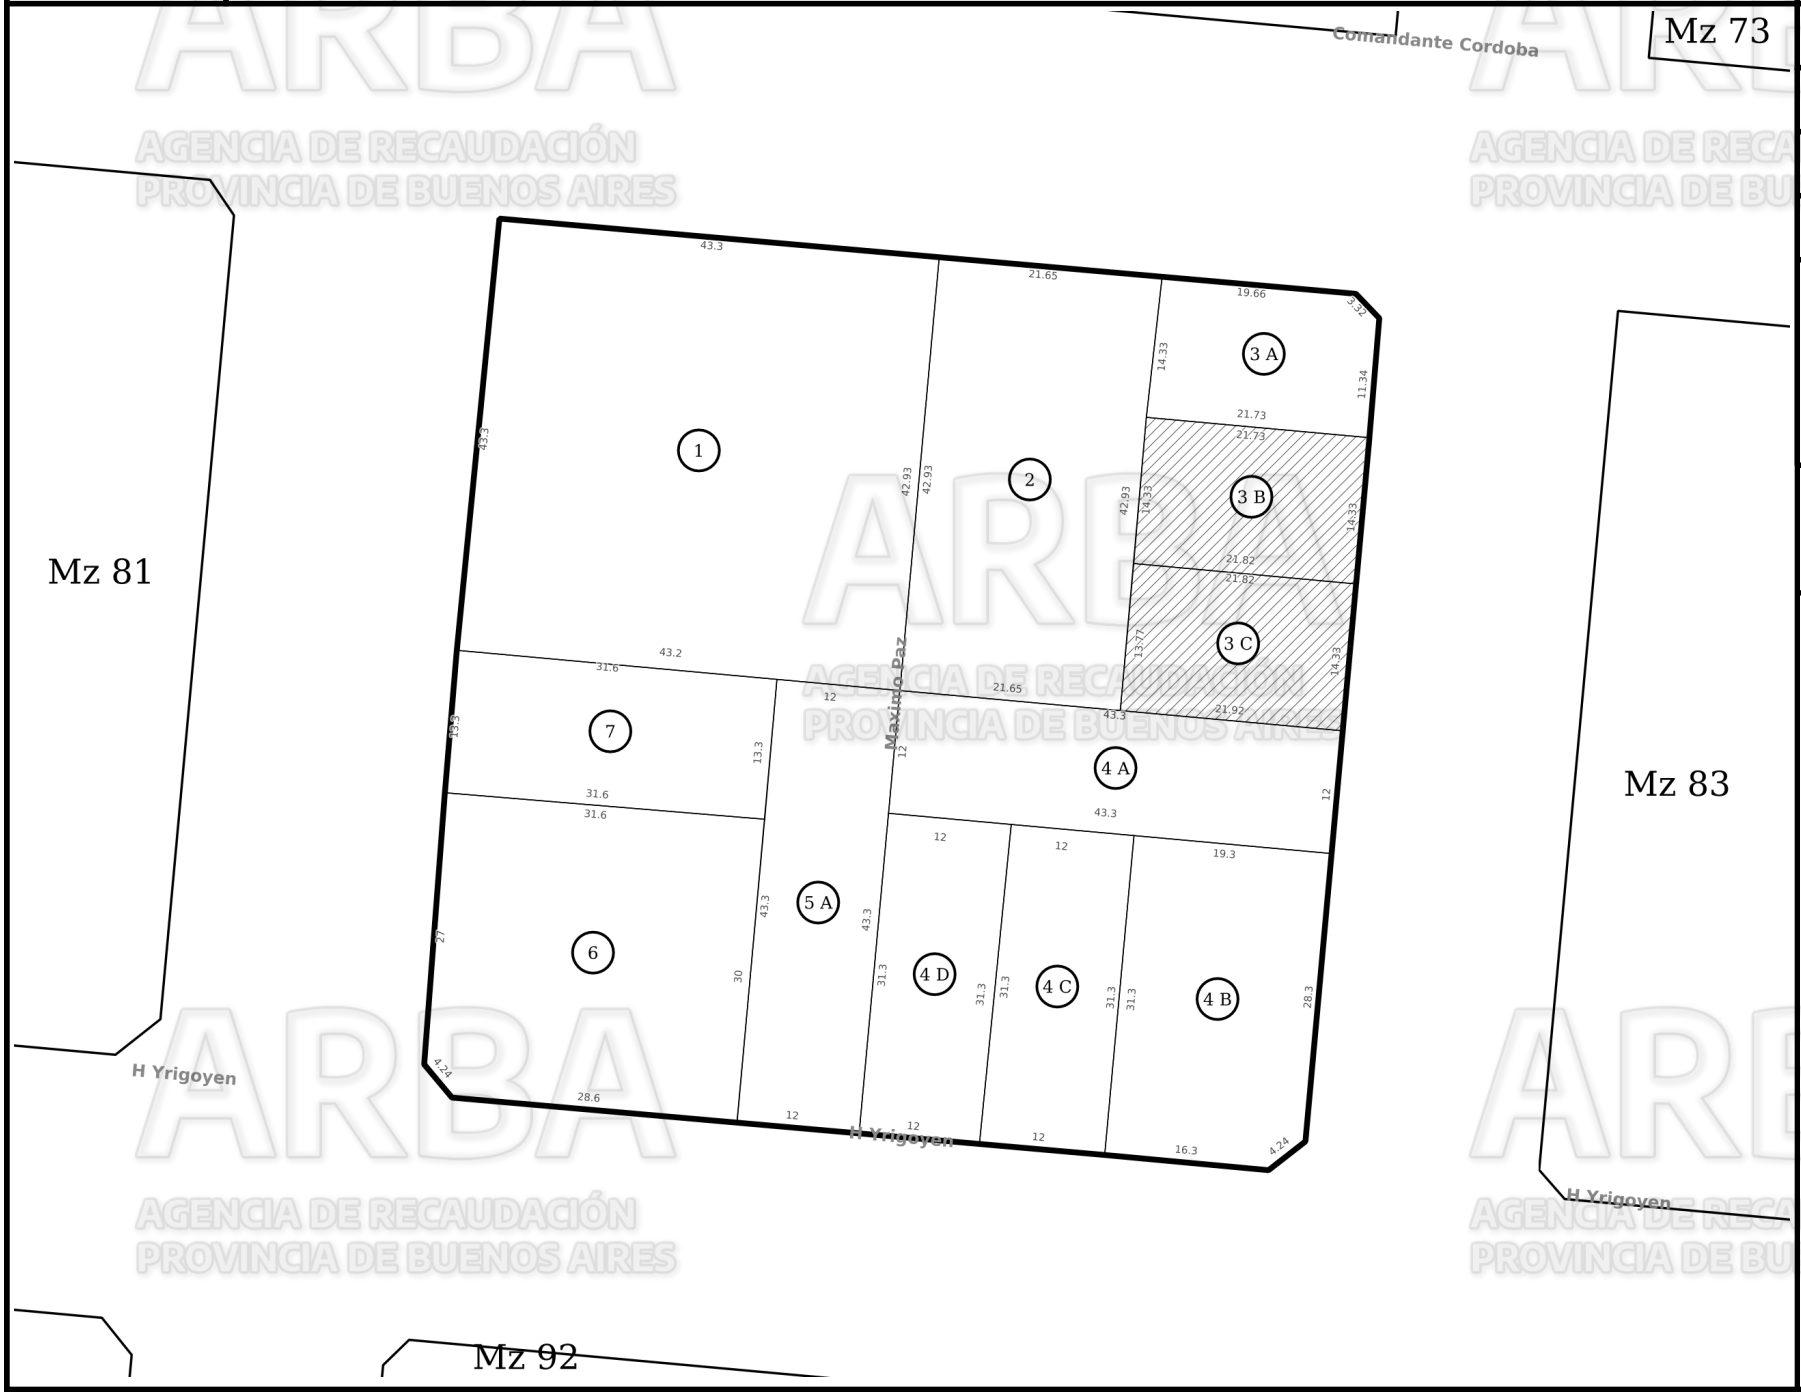


| NOMENCLATURA | |
|---|---|
| Cir. 1 | Sec. A |
| Ch. | Qt. |
| Fr. | Mz. 82 |

N
W E
S

Parcela baldía según catastro

ARBA
AGENCIA DE RECAUDACIÓN
PROVINCIA DE BUENOS AIRES