154

PROVINCIA DE BUENOS AIRES
MINISTERIO DE HACIENDA, ECONOMÍA Y PREVISIÓN
DIRECCIÓN INMOBILIARIA

CATASTRO PARCELARIO

PARTIDO: Gral PINTO

UBICACION

TITULO		CATASTRO	
Cuartel		Circuns.	I
Sección		Sección	B
Chacra		Chacra	
Quinta		Quinta	54
Fracción		Fracción	
Manzana		Manzana	54 b

SUPERFICIES

Parc.	Superficie	Parc.	Superficie	Parc.	Superficie
5	220.~				
6a	622.50				
6b	411.95				
6c	404.25				
1a	423,50				
~~1b~~	~~1461,62~~				
1c	428.				
1d	1.033.62				

SUPERFICIE TOTAL

PLANOS AGREGADOS

DIRECCION GEODESIA 44-48-58

REGISTRO PROPIEDAD 1669/913

OTRAS FUENTES

PLANOS MODIFICATORIOS

44-44-76 (1c/d)
77-56-67 (5/6c)
44-43-70 (12-b)

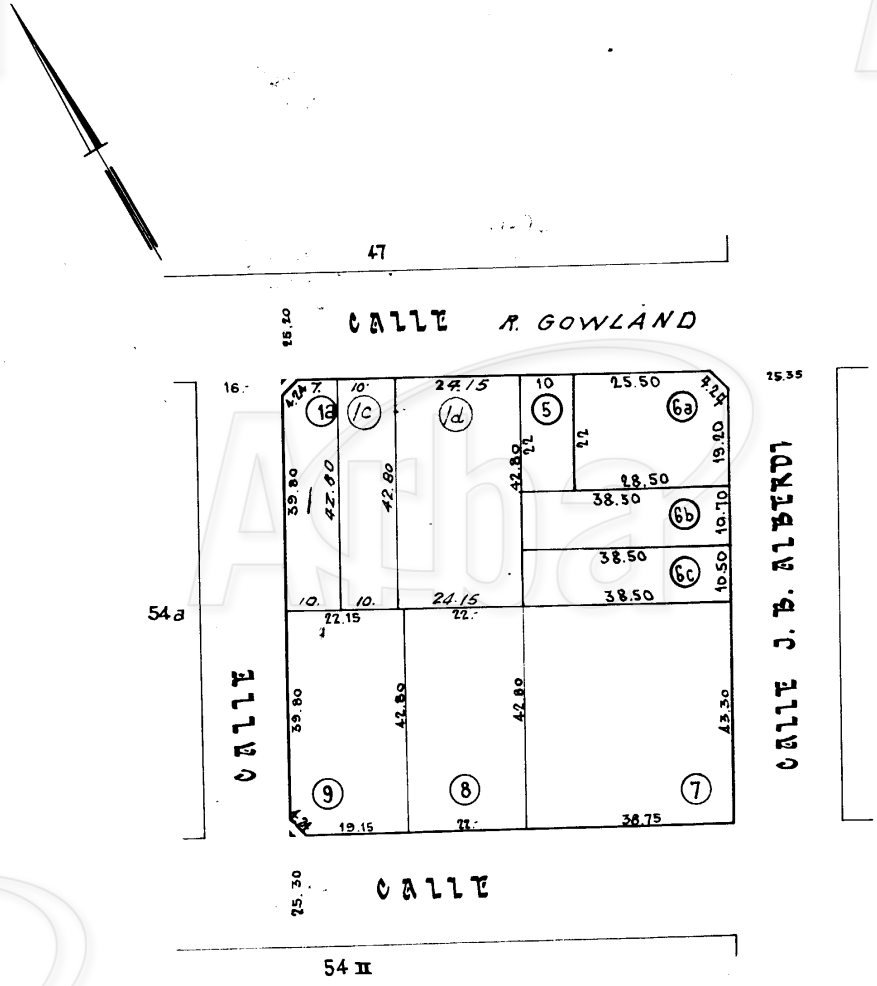

Plano Posesión 44-44-74, afecta P. 7.-

CALLES	SERVICIOS SANITARIOS				AFIRMADOS	MEJORAS	MUNICIPALES	DIBUJO
	AGUA	FECHA	CLOA.	FECHA				CONTROL

ESCALA 1: 1000

CONTROL
FIRMA
FECHA
REGISTRO Nº

000185

PLANCHETA DIGITAL

Partido 44
General Pinto

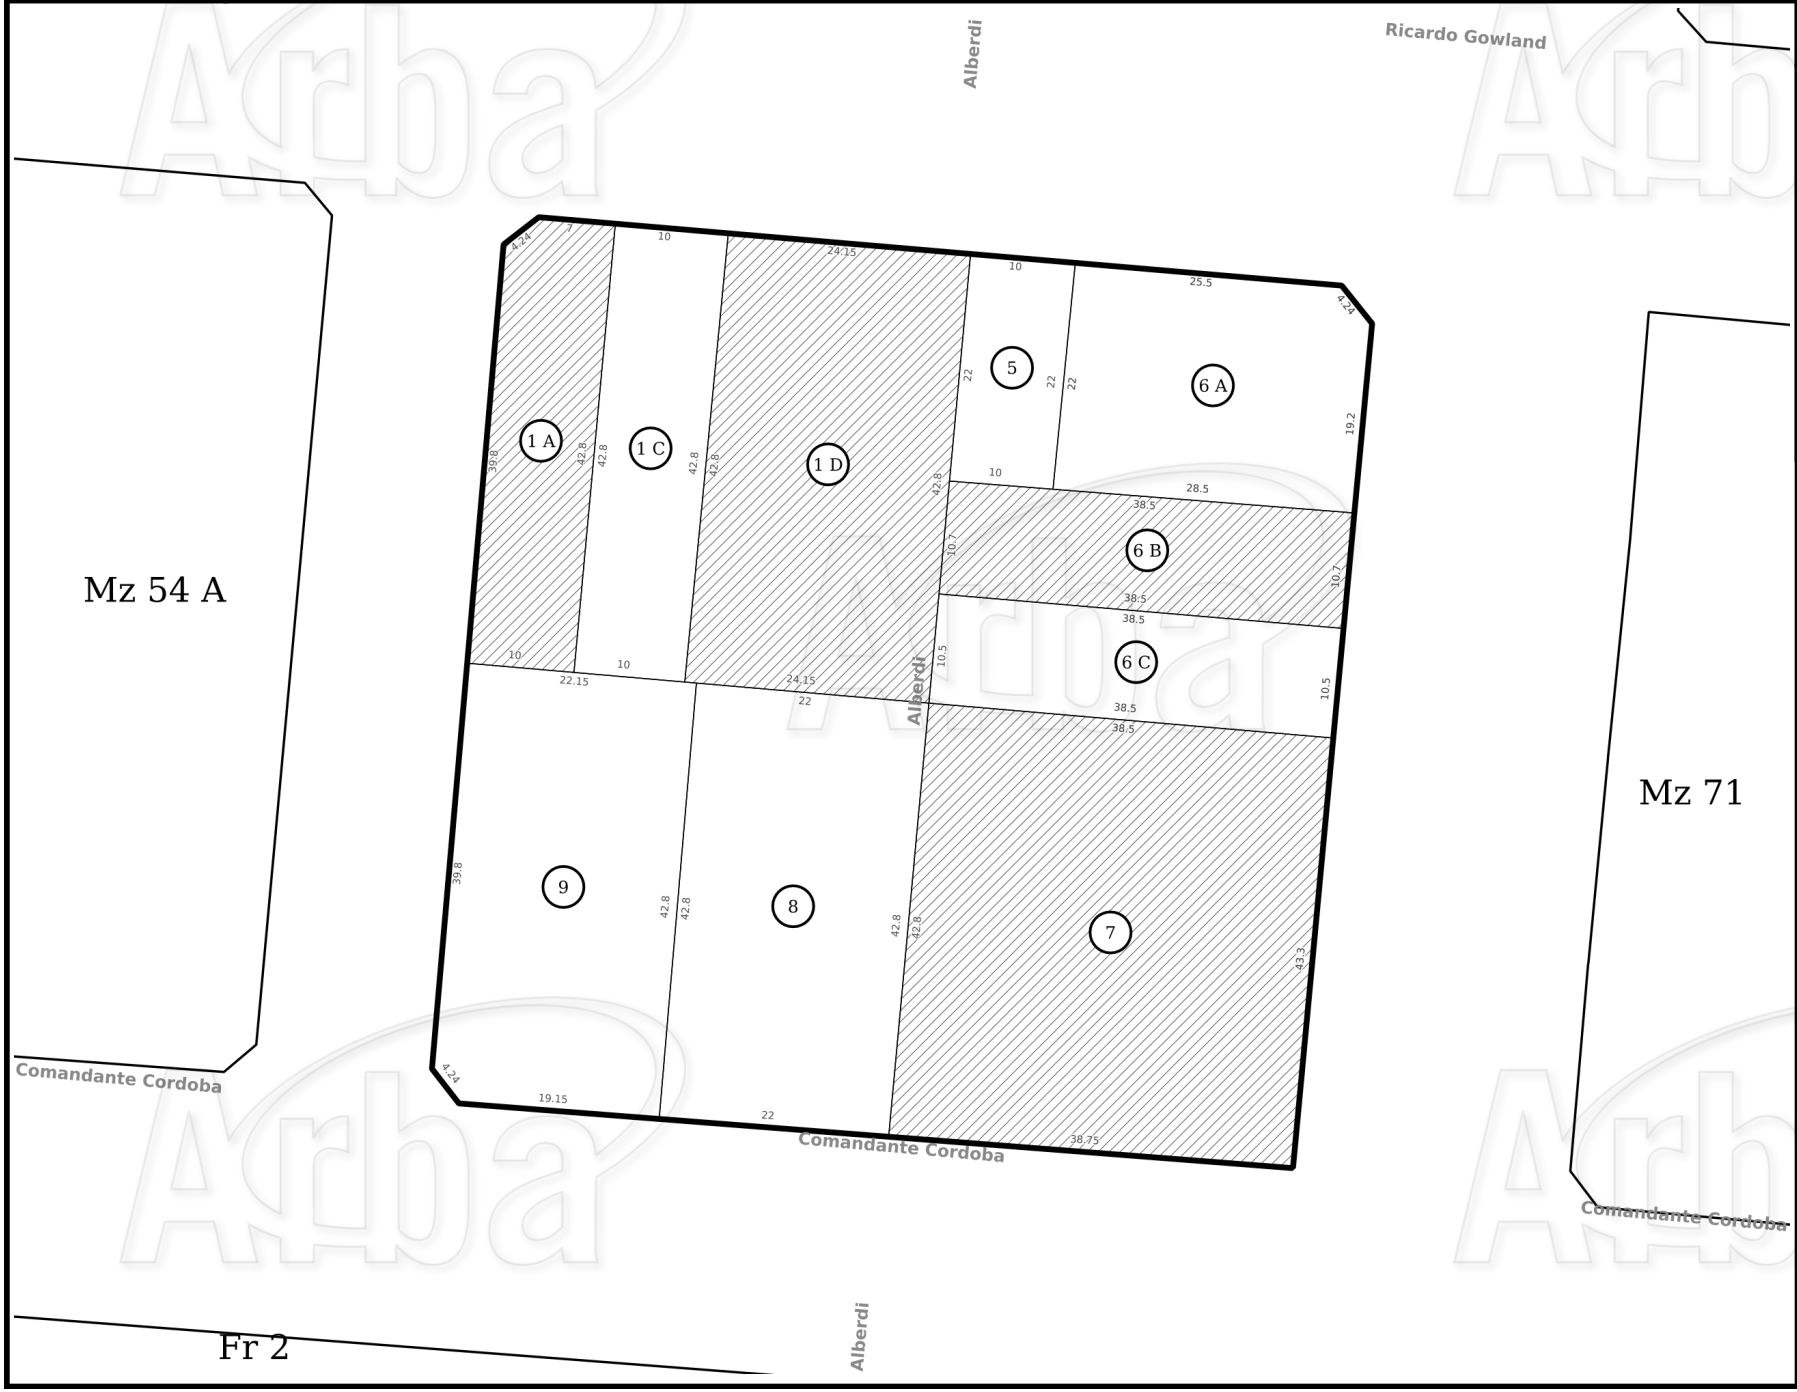

NOMENCLATURA

Cir. 1	Sec. B
Ch.	Qt. 54
Fr.	Mz. 54 B

N
W E
S

Parcela baldía según catastro